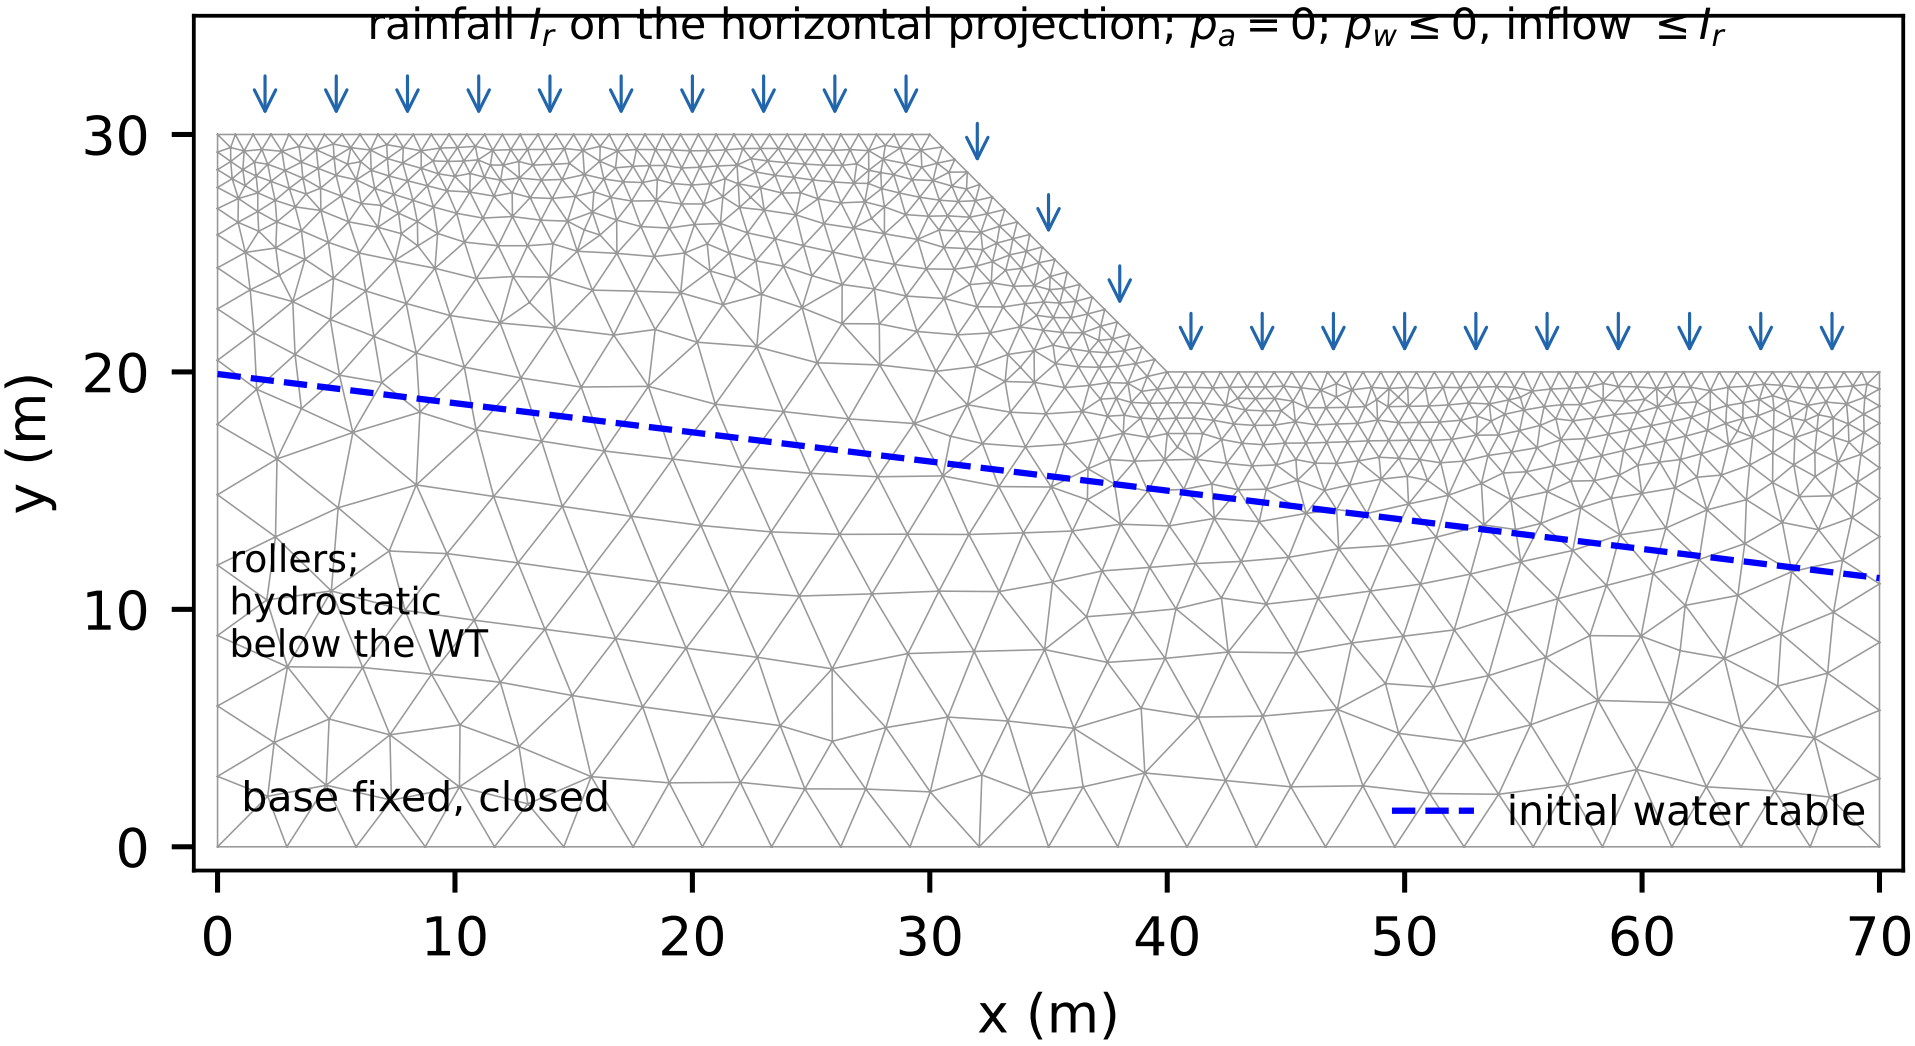
rainfall I_r on the horizontal projection; $p_a = 0$; $p_w \leq 0$, inflow $\leq I_r$
rollers;
hydrostatic
below the WT
base fixed, closed
initial water table
y (m)
x (m)
0
10
20
30
40
50
60
70